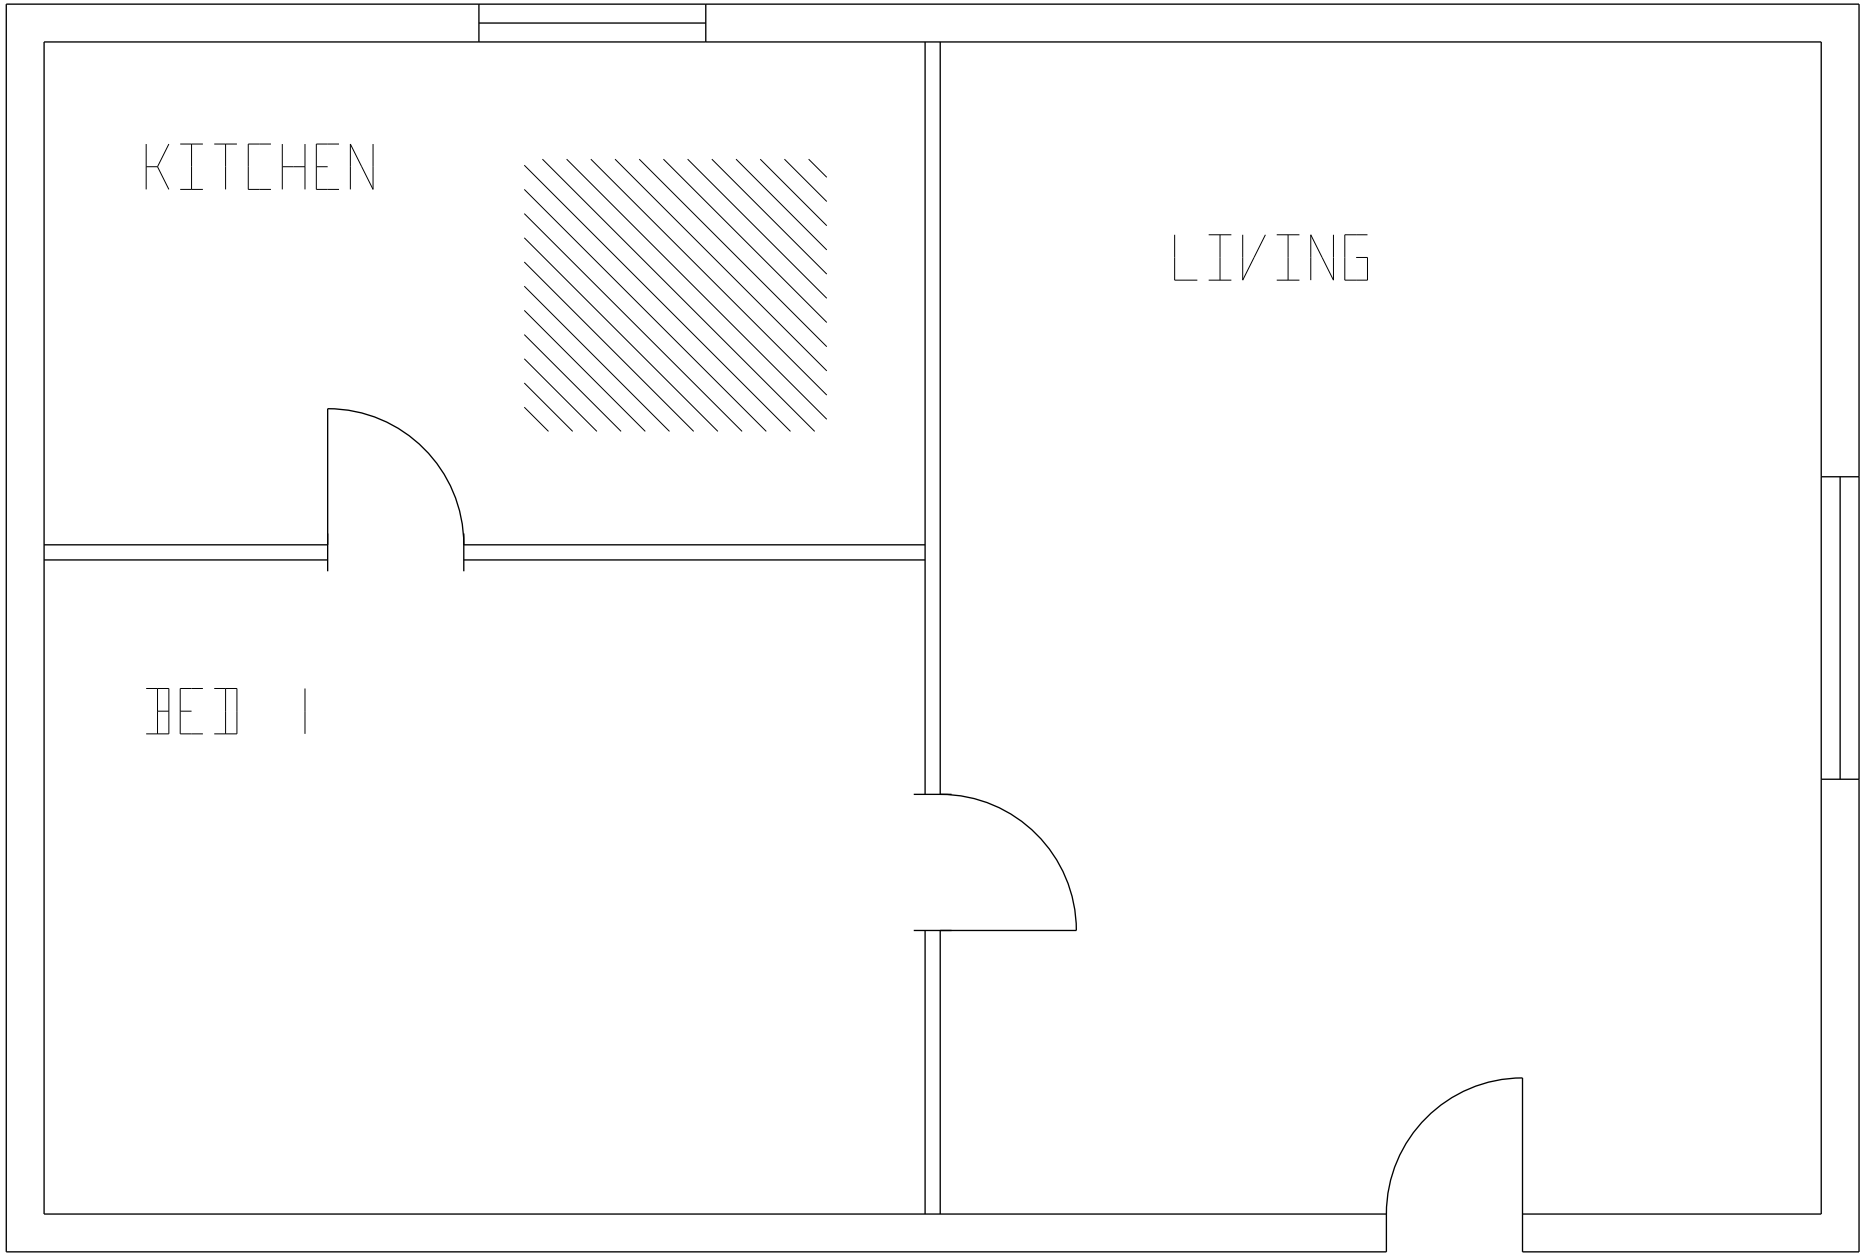
KITCHEN
LIVING
BED 1

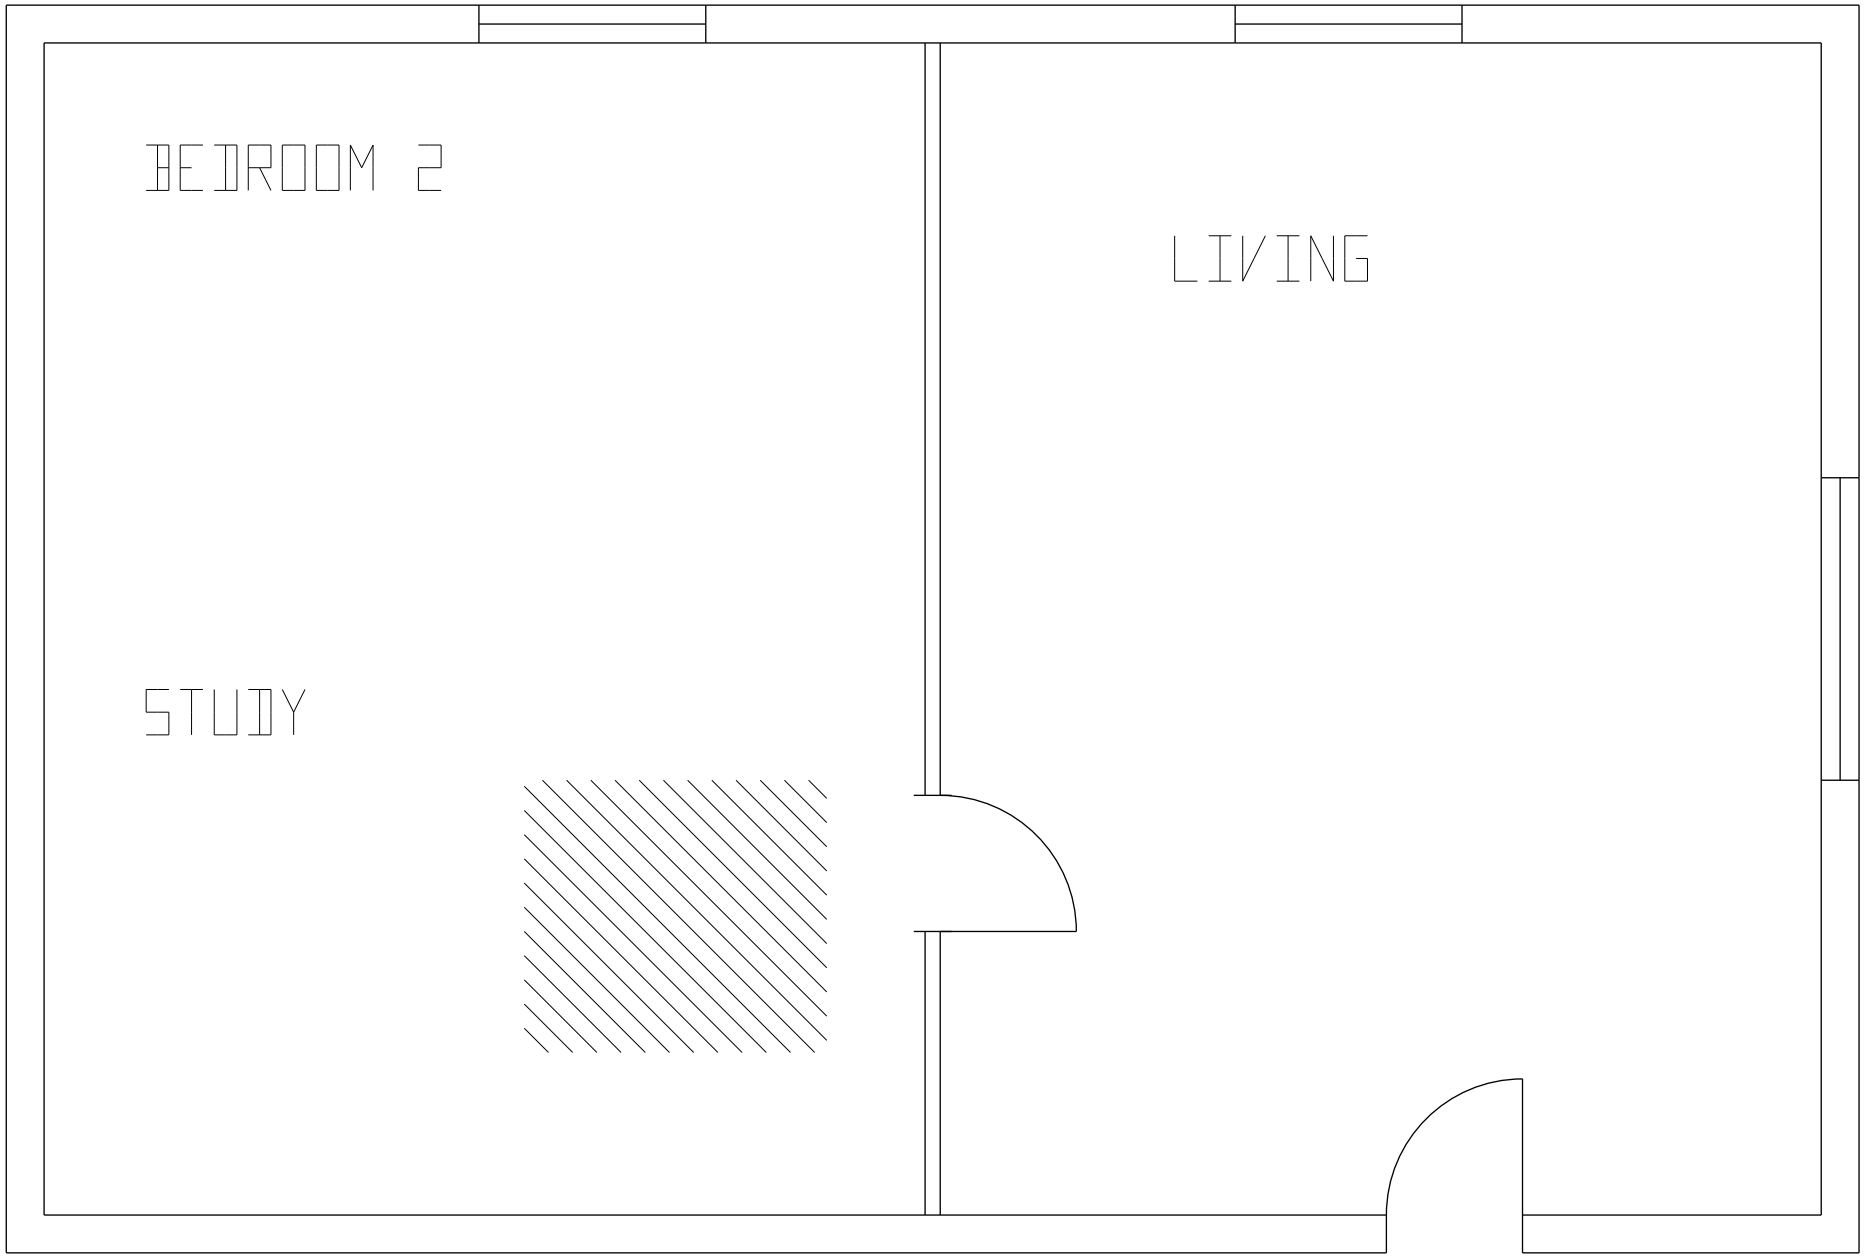
BEDROOM 2
LIVING
STUDY